



# EIRA HOUSE

## .INFO

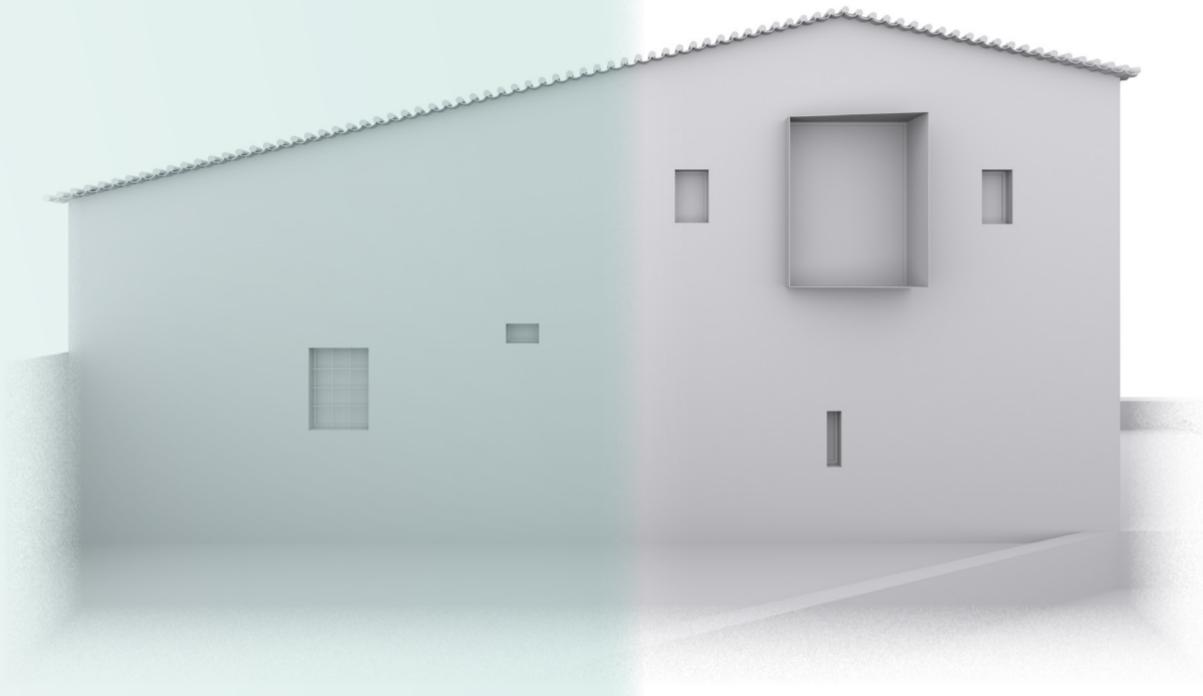



LATO OVEST

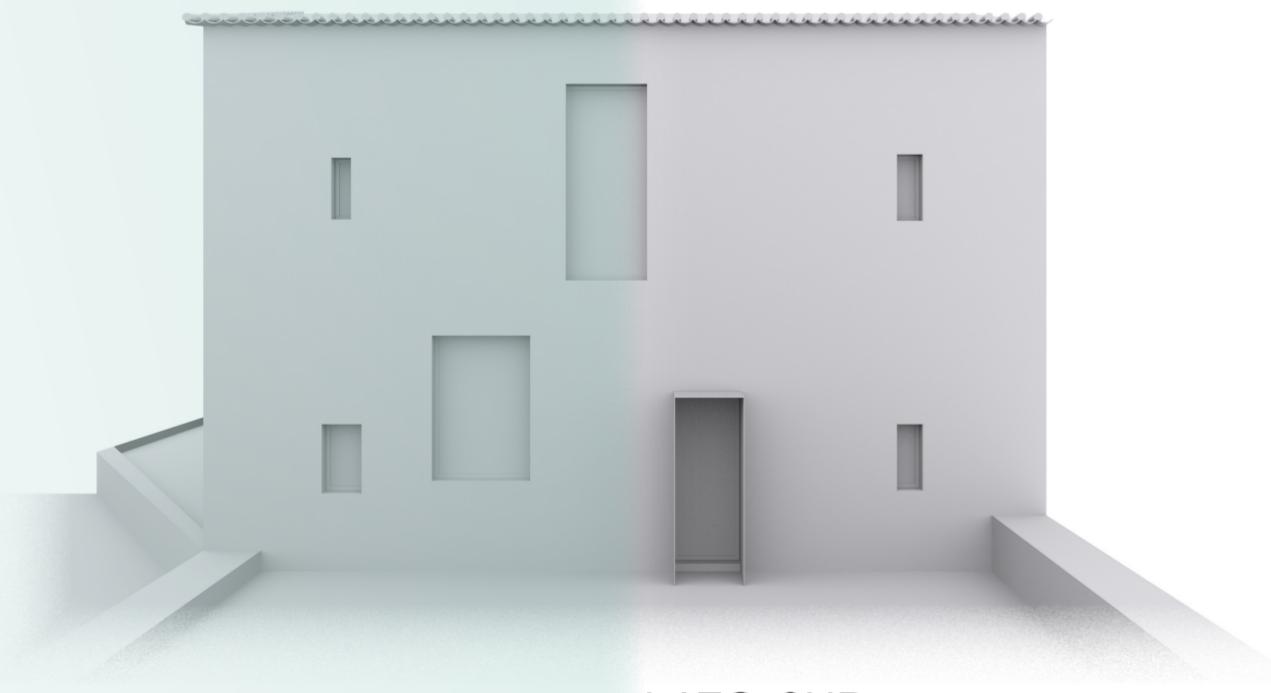

LATO SUD

Architects : AR Studio Architects  
Location : Vale de Cambra, Portugal  
Area : 400.0 m<sup>2</sup>  
Project Year : 2016


Colaborators : João Ferreira, Soraia Oliveira  
Architects in Charge : Daniel Antunes  
e Ricardo Russo  
Contractor : Rogério Martins Construções

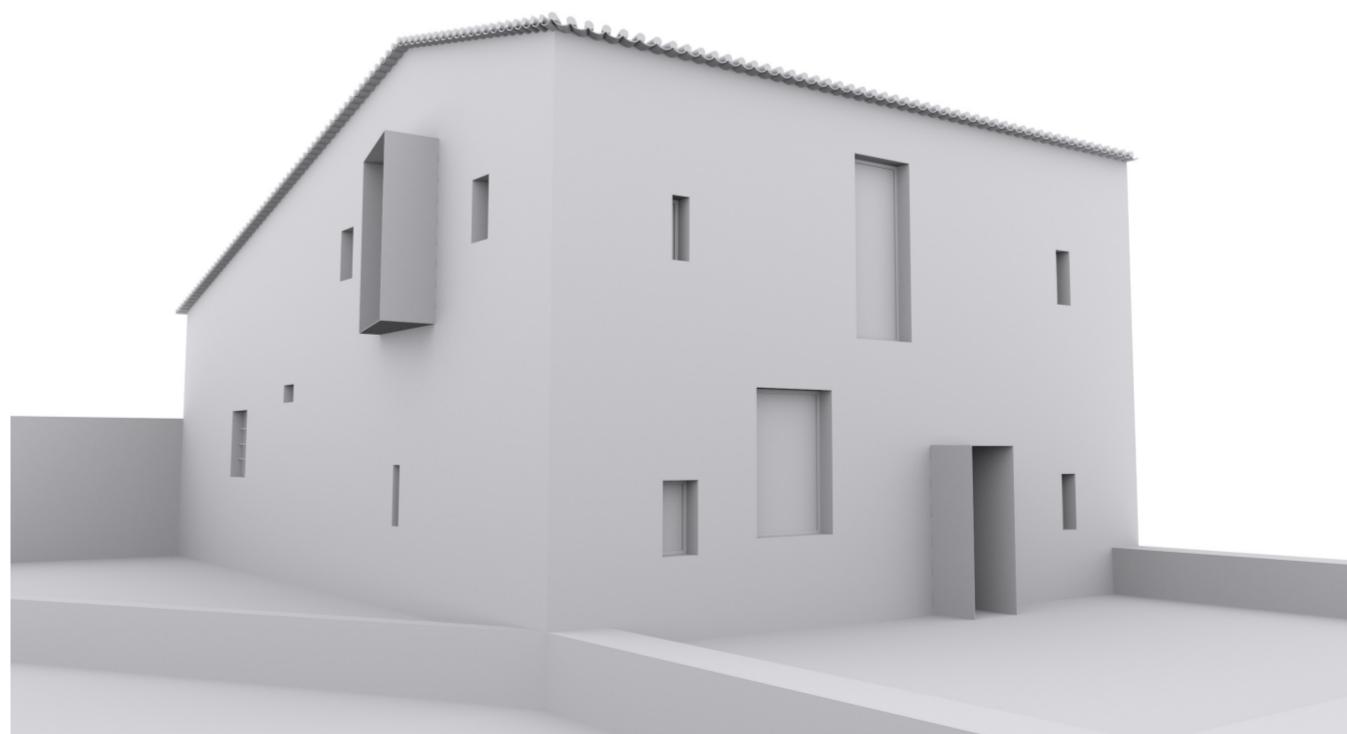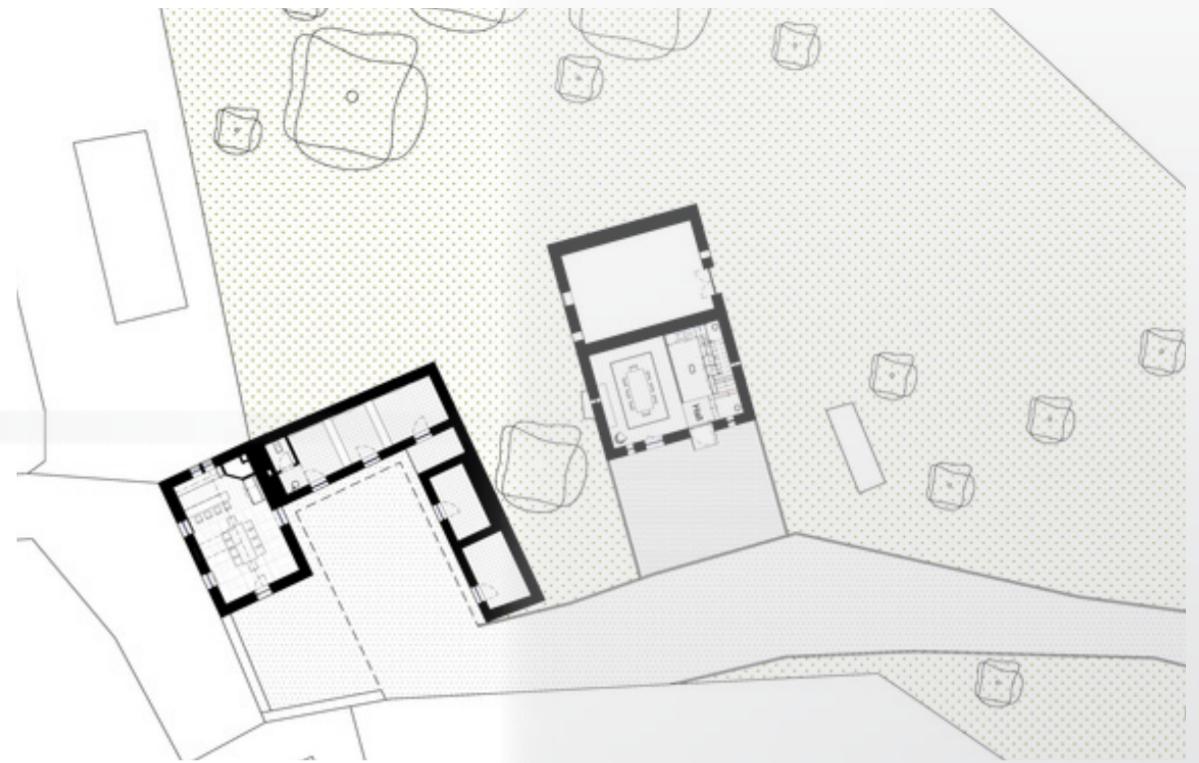

## . INTERNI





**Eira House** è stata frutto di un progetto di ristrutturazione di una precedente costruzione. La casa secolare era gravemente degradata, e sentiva l'esigenza di un intervento che potesse far rivivere la memoria dello stato originale, e al tempo stesso tenendo presente le esigenze attuali. Il proprietario voleva una residenza dove potesse trovare un ambiente familiare e tradizionale, in cui gli amici sono sempre i benvenuti, non tralasciando però il suo lato più creativo ed irriverente.

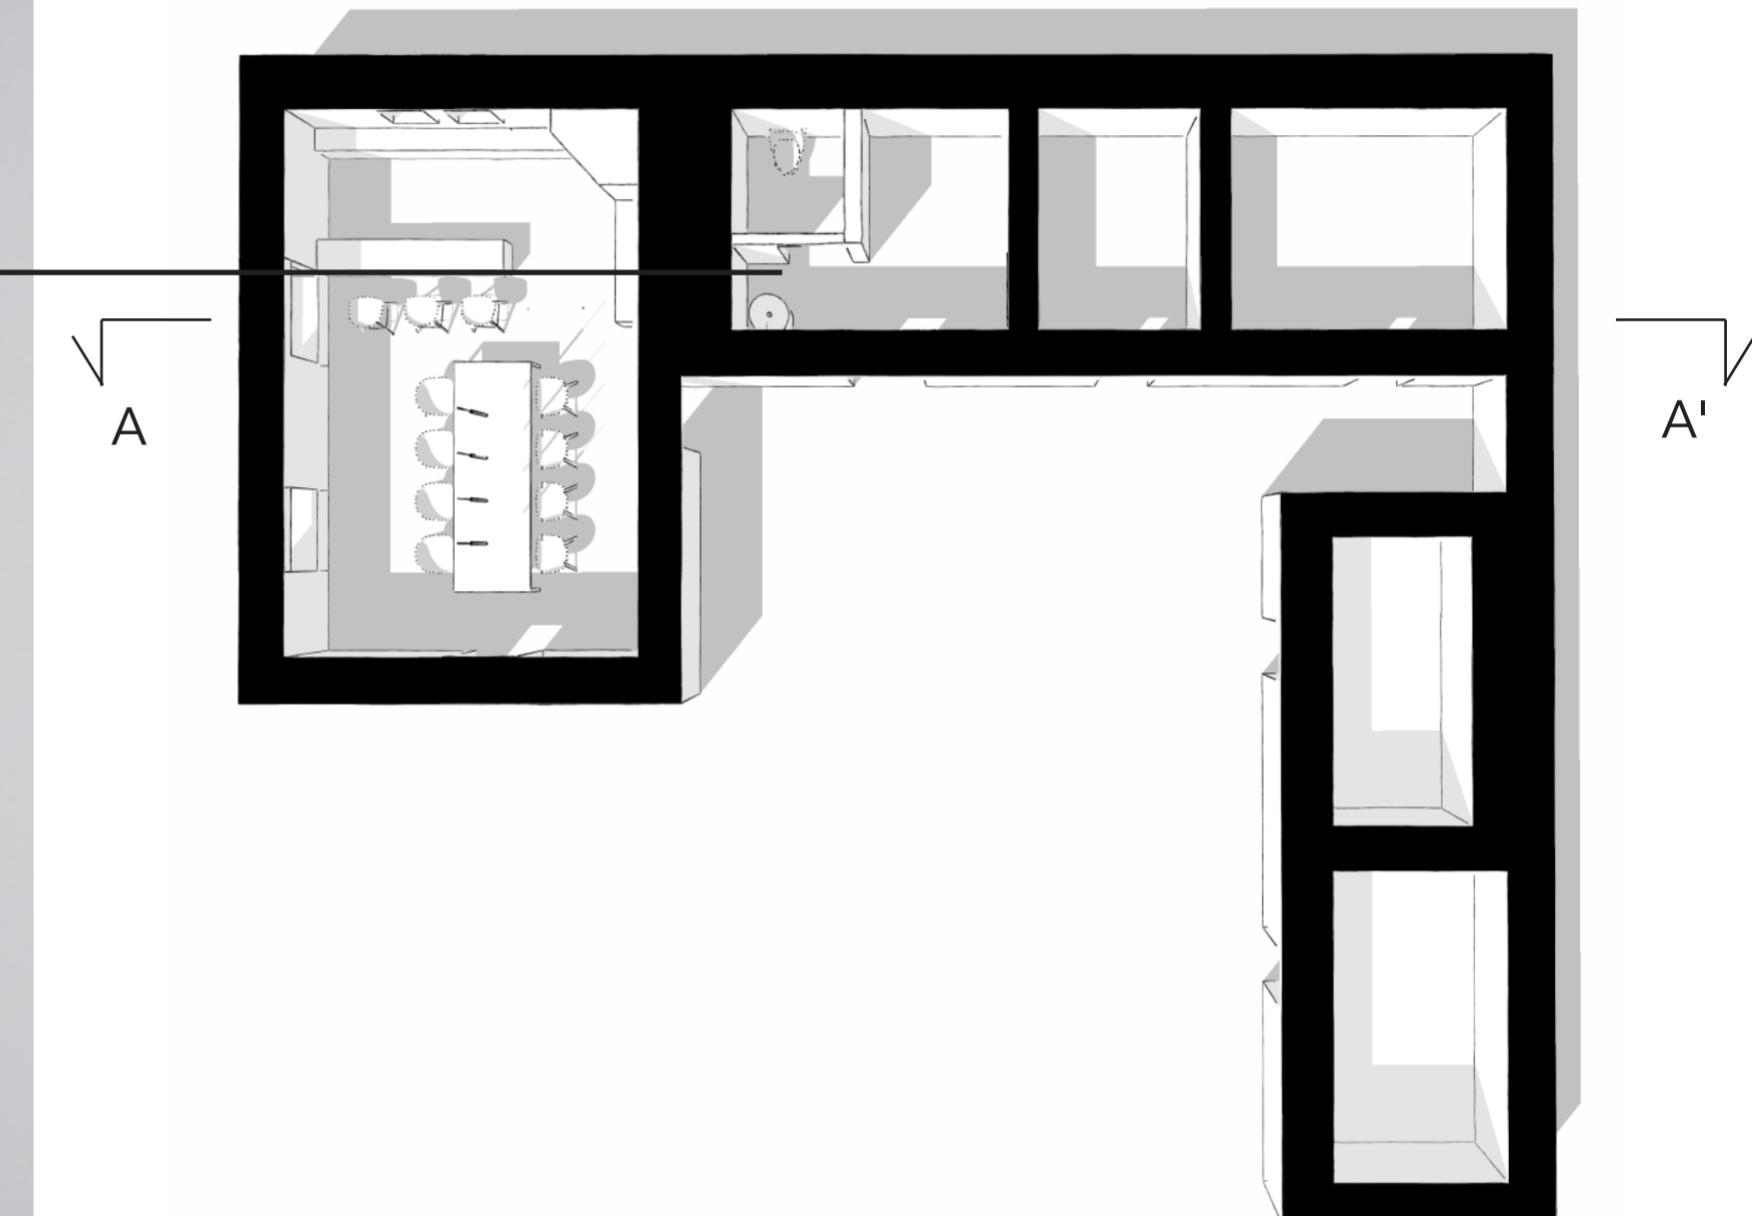

La ristrutturazione riguarda due blocchi. Nel primo troviamo un'area precedentemente utilizzata per le stalle degli animali, trasformata in una zona conviviale, con cucina e sala da pranzo, un bagno, e alcune zone che mantengono il tratto originale e sono di uso conviviale.



Nel secondo blocco si trovano gli spazi privati. La sala da pranzo e la cucina sono divisi da un elemento che consente la permeabilità visiva. L'armadio della cucina è un elemento continuo di collegamento tra i due piani che conferisce uniformità agli spazi. Il soggiorno presenta un'area di lettura che è come se si staccasse dall'edificio per abbracciare la natura circostante. Inoltre il piano superiore ha un accesso diretto al giardino sul retro che presenta maggiore altezza.

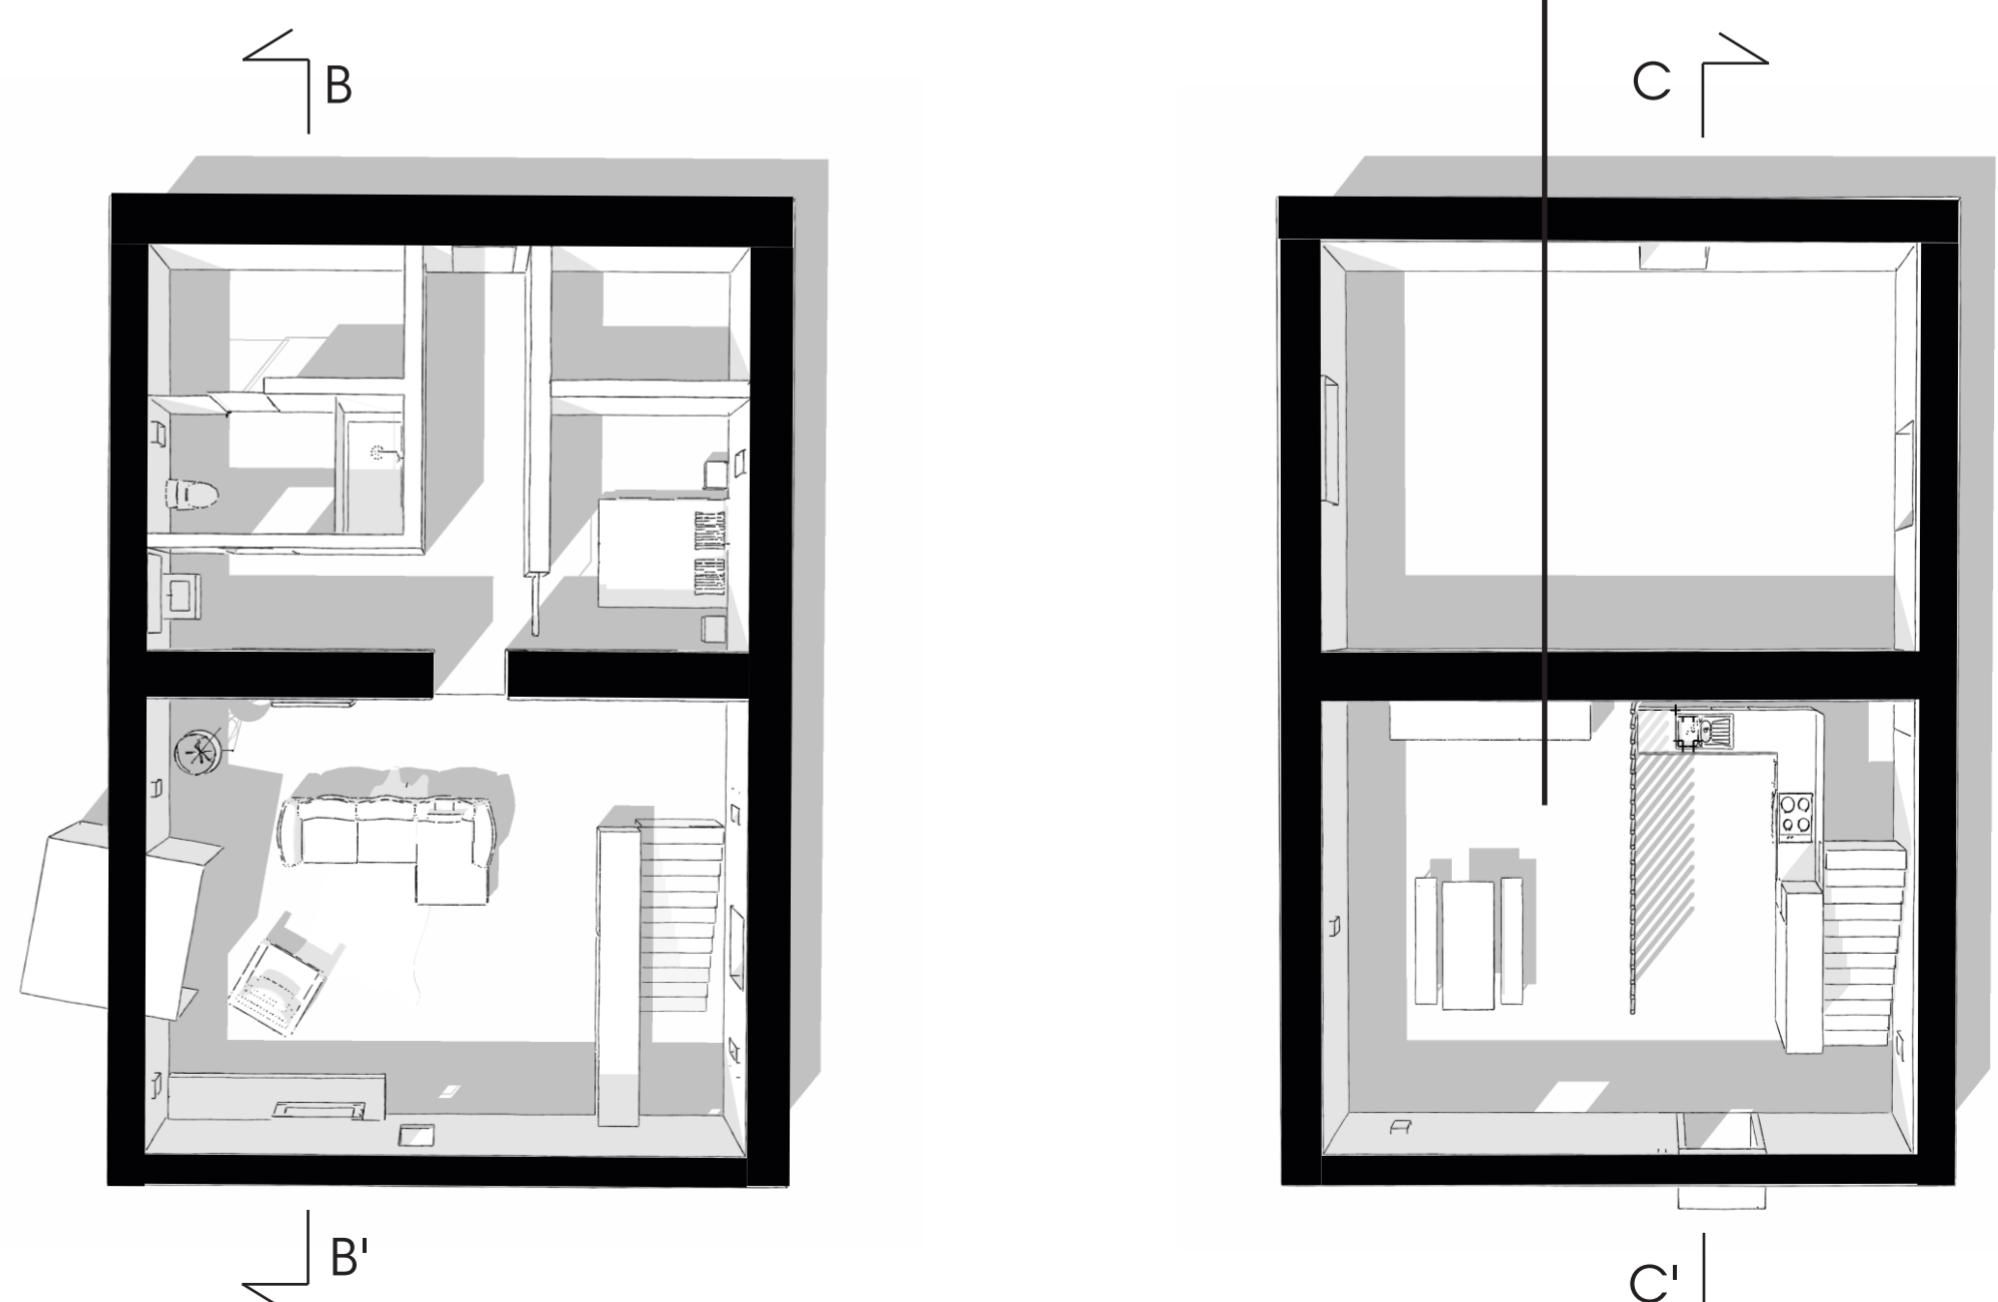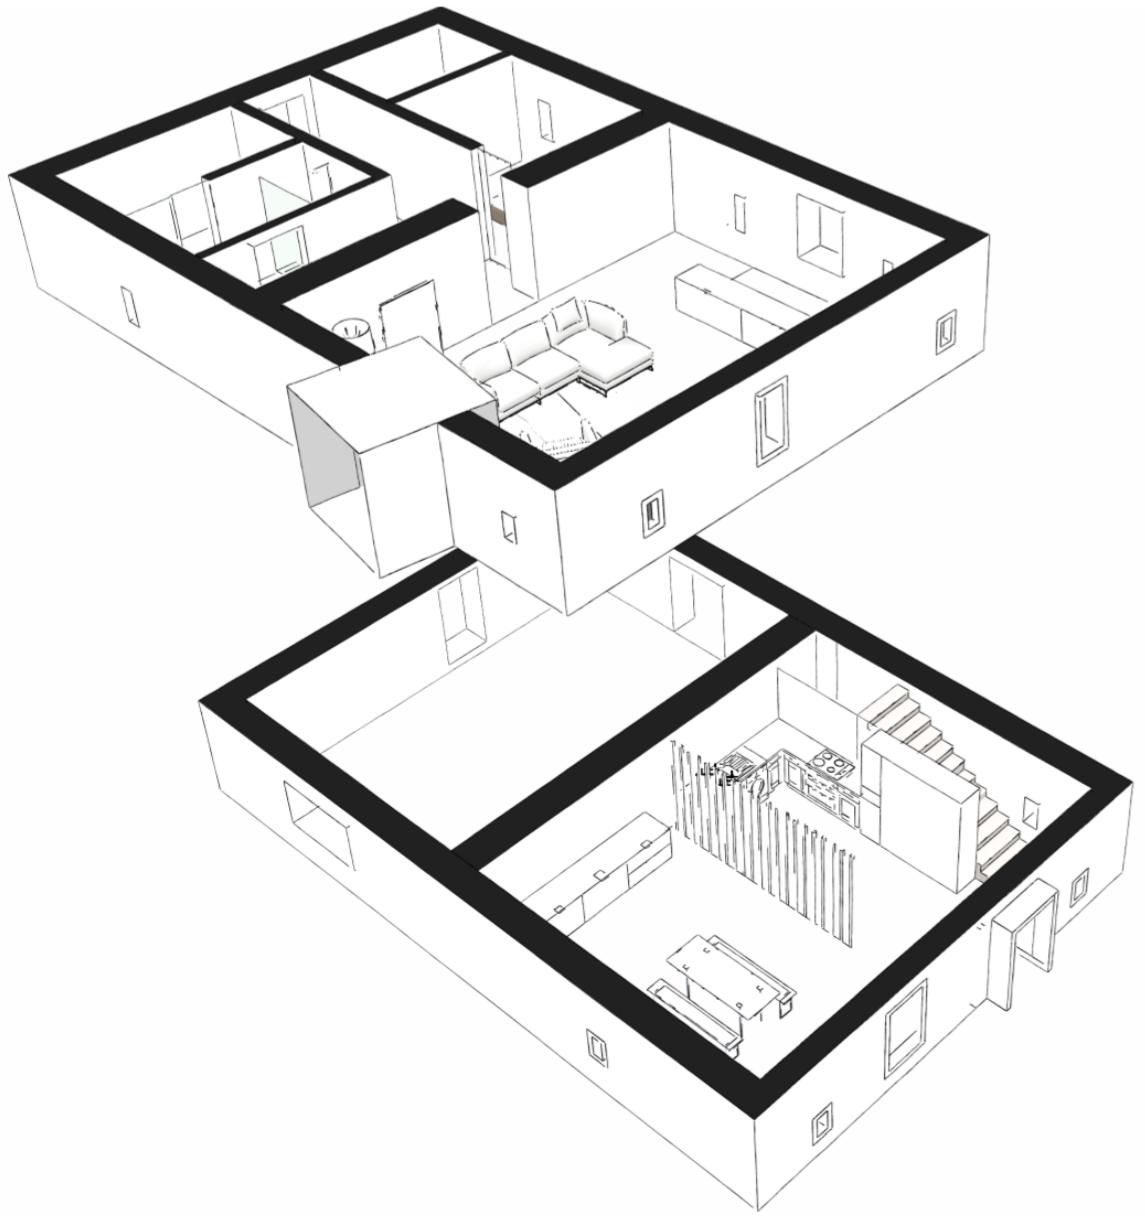

# SEZIONI E AMBIENTI




LIVING  
1



BAGNO  
2




ZONA  
COMUNE  
3

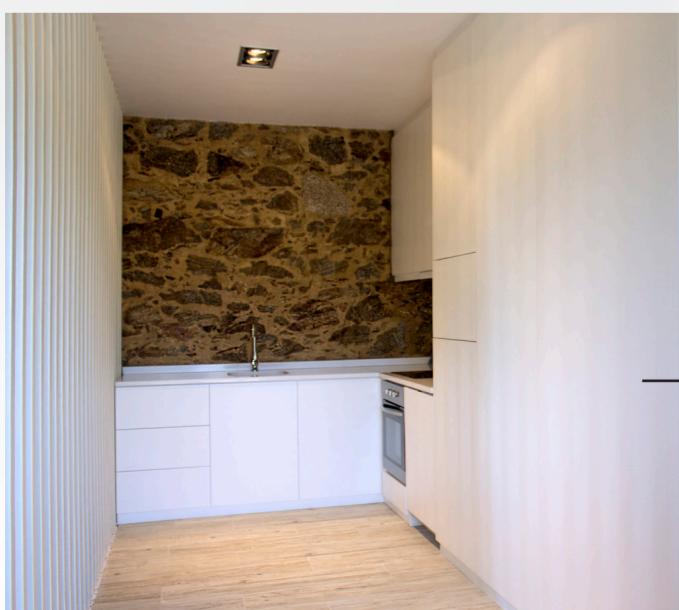

CUCINA  
4



A-A'

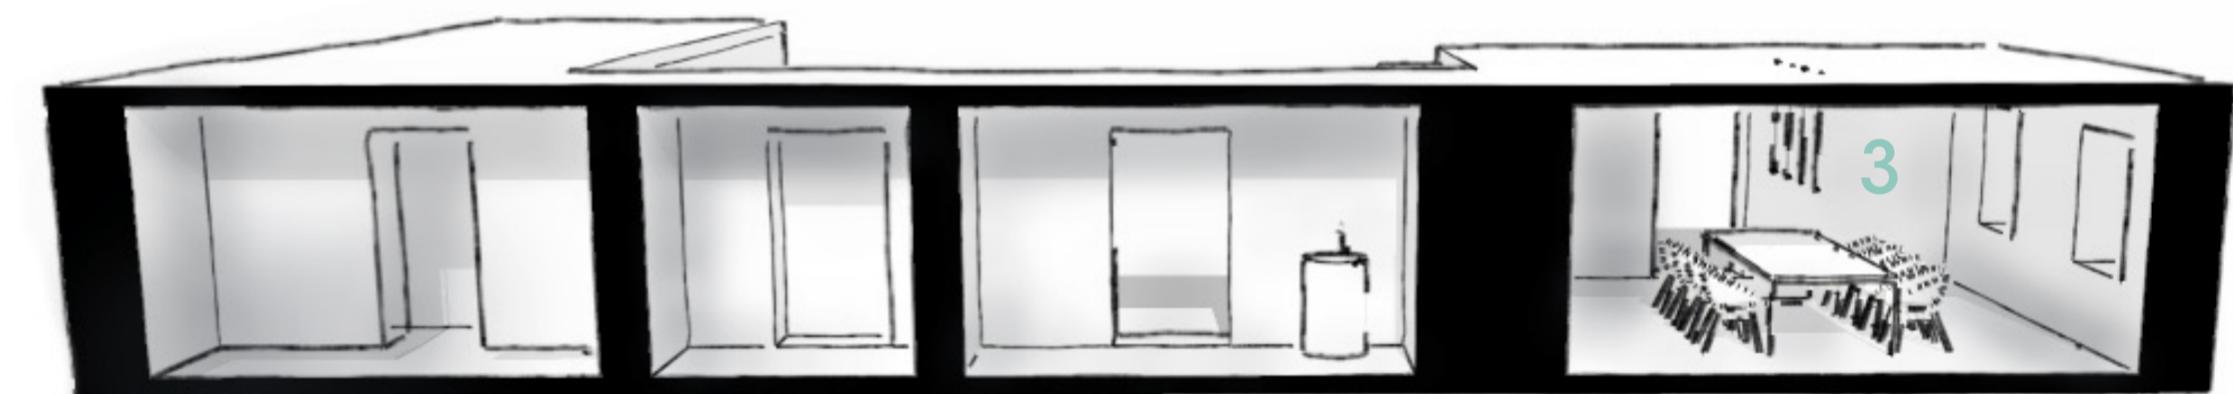

B-B'



C-C'